# HULL / EXTERIOR ELEVATIONS

Physical wooden prototype - exterior envelope remains separate from the linked carrier.

## 01 ENTRANCE-SIDE ELEVATION

30 frame bays at 15 ft pitch. Door: 12 ft wide x 10 ft high; sill H-z 16 ft 6 in.

## 02 END ELEVATION

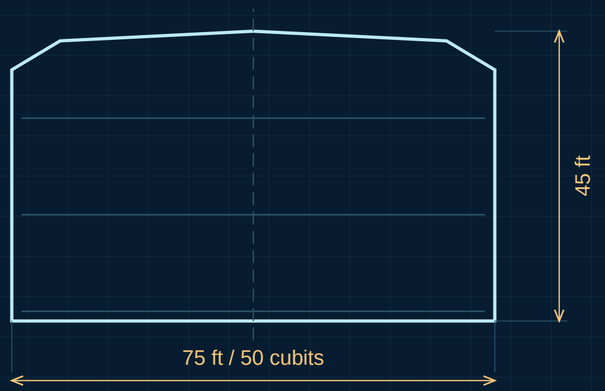


### HULL DATUM

H-x 0 = outside stern face
H-x 450 = outside bow face
H-y 0 = longitudinal centerline
H-z 0 = bottom of outside envelope

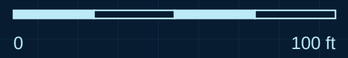


### MEASURED ENVELOPE

450 x 75 x 45 ft outside
300 x 50 x 30 cubits
Three ordinary stories

### ESTABLISHED SHAPE

Bluntly rounded ends in plan.
Shallow upturn below the ends.
Low crown within 45 ft height.
Exact curve radii are unspecified.

### MATERIAL REGISTER

Timber frame, wooden pegs,
keys, wedges and hinges.
Pitch / resin sealing.
No metal hardware in Ark domain.

### DRAWING CONVENTION

Frame ticks show 15 ft spacing.
Dashed lines locate floor levels.
Roof profile is diagrammatic;
no new curvature is asserted.

**BRIAN CHAPMAN SR MSP A+ CIW**

Source: The Ark: An Illustrated Anatomy | Chapters 3-4, 6 | 1 cubit = 18 in = 1.5 ft

Fictional architectural study. Written dimensions govern. Profiles and unspecified construction are diagrammatic.

# HULL / THREE DECK PLANS

Clear-space organization from the atlas; unscheduled room partitions are intentionally left open.

450 ft outside / nominal 447 ft inside before rounded ends

## 01 UPPER STORY / FFL H-z 31.5 ft

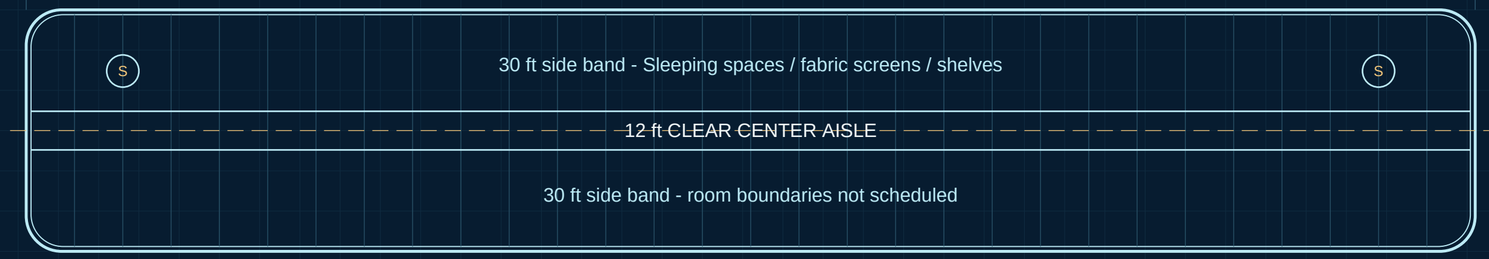


## 02 MIDDLE STORY / FFL H-z 16.5 ft

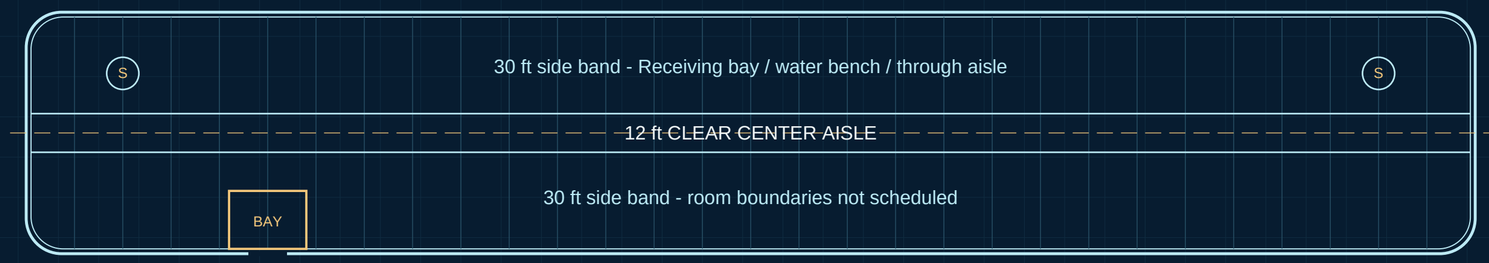


## 03 LOWER STORY / FFL H-z 1.5 ft

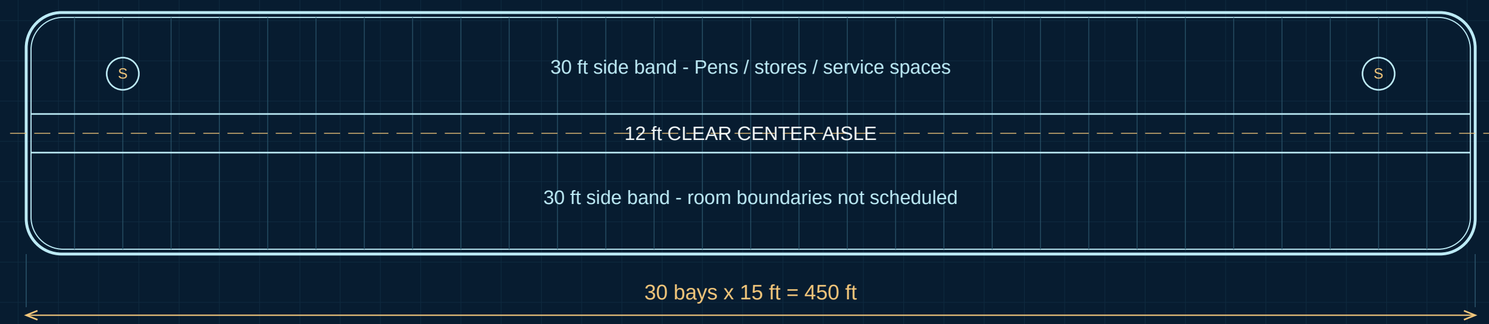


### PLAN WIDTHS

75 ft exterior
72 ft clear between inner sides
12 ft aisle + 30 ft each side
1 ft 6 in side / end allowances

### SYMBOLS

S = stair location near H-x 30 ft and 420 ft; enclosure footprints are not specified.
Amber bay = 24 x 18 ft clear receiving vestibule; location across width shown schematically.

### HEADROOM

Lower: 13 ft 6 in clear
Middle: 13 ft 6 in clear
Upper: 12 ft at roof center
Upper clearance falls at sides.

### PARTITION STATUS

These are measured zoning plans. The book does not give a complete room-by-room hull partition plan. No invented cabin count is added.

BRIAN CHAPMAN SR MSP A+ CIW

Source: The Ark: An Illustrated Anatomy | Chapters 4-6 | 1 cubit = 18 in = 1.5 ft

Fictional architectural study. Written dimensions govern. Profiles and unspecified construction are diagrammatic.

# DETAILS / THRESHOLD AND WOODEN JOINT

Two measured atlas details. The dimensional connection belongs to the fictional story architecture.

## 01 RECEIVING VESTIBULE / PLAN

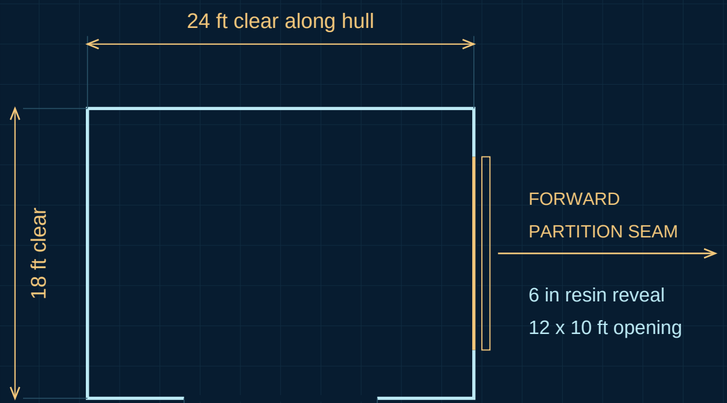


## 02 TRANSFER APPROACH / UNFOLDED PROFILE

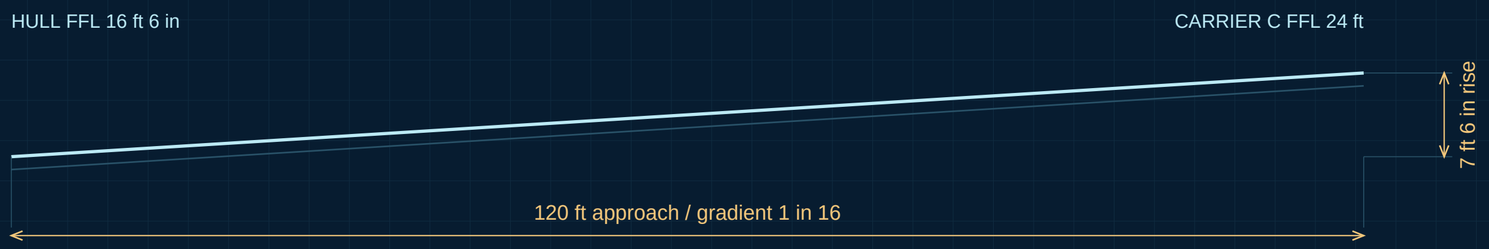


Folded transfer space; separate from the 780 ft carrier length. Vertical rise exaggerated for clarity.

## 03 JOINT / FACE STUDY

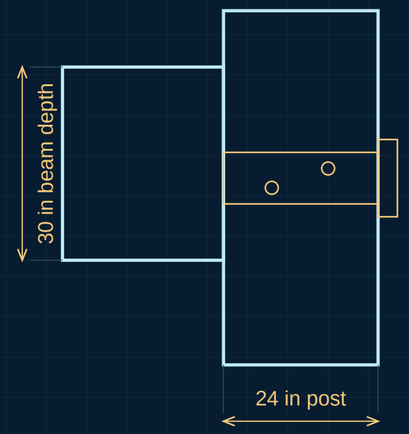


Beam width 18 in (out of plane).
Peg spacing / key length not specified.

### THRESHOLD REGISTER

Side door center: H-x 75 ft
Sill: H-z 16 ft 6 in
Vestibule: 24 x 18 x 10 ft clear
Seam sits in forward partition.

### JOINT REGISTER

Post: 24 x 24 in
Beam: 18 in wide x 30 in deep
Through-tenon: 8 in wide
Two wooden pegs: diameter 2 in
Hardwood key: 3 in thick

### DETAIL LIMITS

Joint is a schematic face study.
Tenon depth, edge distances and peg spacing are not scheduled.
No structural rating is implied.

### SPATIAL CONNECTION

The physical hull does not enlarge.
A registered seam joins another coordinate space with its own dimensions and floor levels.

**BRIAN CHAPMAN SR MSP A+ CIW**

Source: The Ark: An Illustrated Anatomy | Chapters 6-7, 10 | 1 cubit = 18 in = 1.5 ft

Fictional architectural study. Written dimensions govern. Profiles and unspecified construction are diagrammatic.

# CARRIER / COMMON SPINE AND 24 STATIONS

Carrier coordinate space C - lengthwise copy of the tower ordering; six occupied decks.

## 01 DECK C / FFL C-z 24 ft

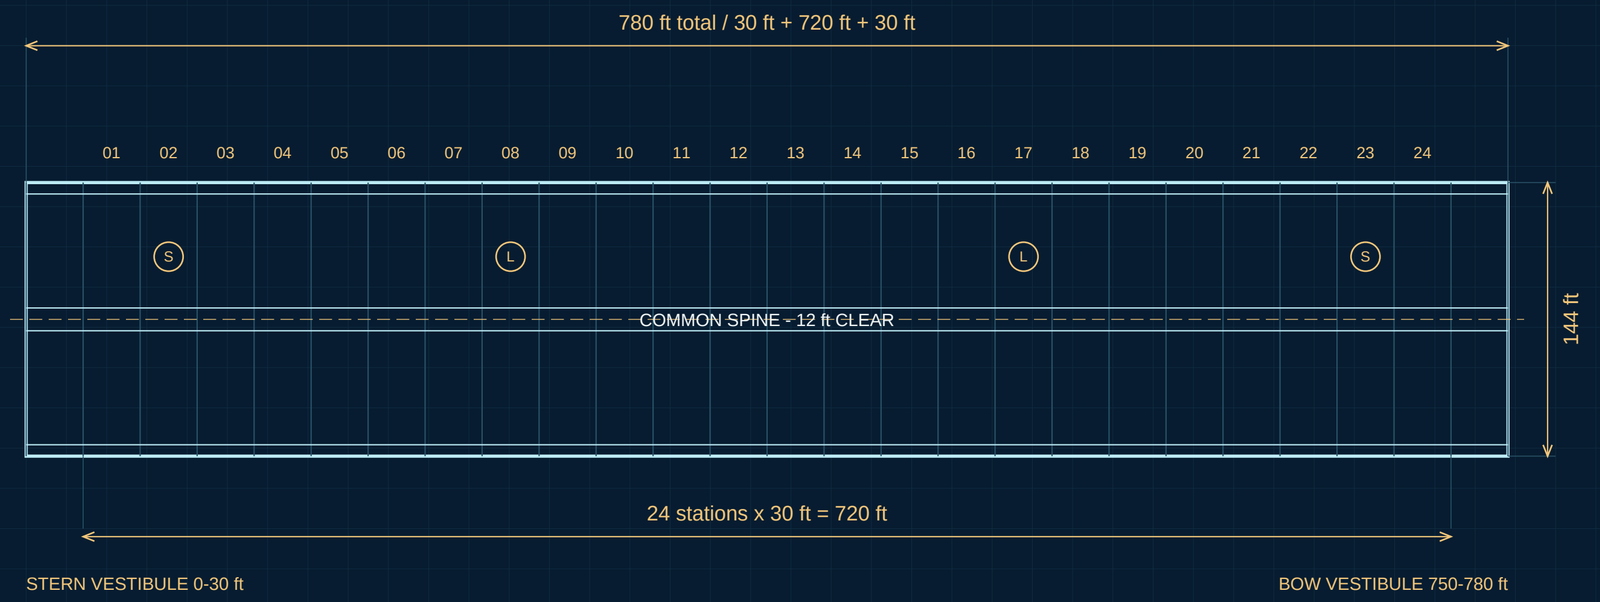


### STATION DIRECTORY / representative primary functions

S01 Arrival
S02 Stern stair
S03 Receiving
S04 Workshop
S05 Stores
S06 Water
S07 Rest
S08 Lift / refuge
S09 School
S10 Garden entry
S11 Households
S12 Table hall
S13 Kitchen
S14 Laundry / bath
S15 Family rooms
S16 Archive
S17 Forward lift
S18 Animal care
S19 Contact prep
S20 Harbor entry
S21 Registry
S22 Reserve rooms
S23 Bow stair
S24 Observation

### PLAN REGISTER

C-x 0-780 ft
C-y -72 to +72 ft
Station zone: x 30-750 ft
Frame pitch: 30 ft

### CROSS-WIDTH BANDS

6 ft outer service / frame strip
60 ft usable side band
12 ft central aisle
60 ft usable side band
6 ft outer service / frame strip

### CIRCULATION

S = protected stair, S02 / S23
L = assisted lift, S08 / S17
Symbols locate stations; their footprints are diagrammatic.

### ROOM PLANNING

Typical cabin: 12 x 18 ft clear
Separate washroom: 4 x 6 ft
Cabin door: 3 ft 6 in clear
Directory names do not imply identical rooms on every deck.

**BRIAN CHAPMAN SR MSP A+ CIW**

Source: The Ark: An Illustrated Anatomy | Chapters 9-12 | 1 cubit = 18 in = 1.5 ft

Fictional architectural study. Written dimensions govern. Profiles and unspecified construction are diagrammatic.

# SECTIONS / SIX DECKS AND THREE STORIES

Compare separate coordinate spaces. Both sections use the same graphic scale: 3 points per foot.

## 01 CARRIER / TRANSVERSE SECTION

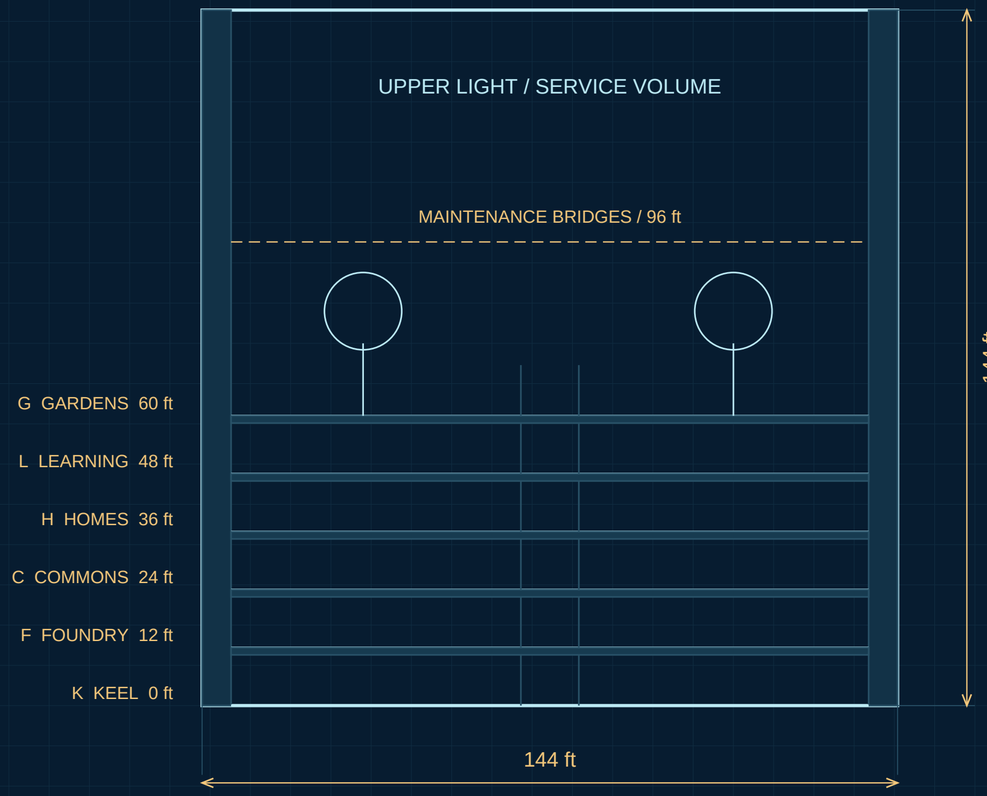


450 ft hull length

780 ft carrier length

Joined by a fictional seam;
these volumes are not nested.

## 02 PHYSICAL HULL

Three stories / same scale

### CARRIER FLOOR SCHEDULE

K 0 / F 12 / C 24 ft
H 36 / L 48 / G 60 ft
12 ft deck pitch
1 ft 6 in floor assembly
10 ft 6 in typical clear height

### UPPER VOLUME

Gardens floor at 60 ft
Selected trellises to 78 ft
Maintenance bridges at 96 ft
Outer crown at 144 ft

### HULL FLOOR SCHEDULE

FFL: 1 ft 6 in / 16 ft 6 in /
31 ft 6 in above hull datum
Lower / middle clear: 13 ft 6 in
Upper clear: 12 ft at center

### SECTION CONVENTION

Planting symbols are illustrative.
No carrier framing sizes are added.
This section follows the atlas,
including its K-floor datum at 0.

**BRIAN CHAPMAN SR MSP A+ CIW**

Source: The Ark: An Illustrated Anatomy | Chapters 4, 10-11 | 1 cubit = 18 in = 1.5 ft

Fictional architectural study. Written dimensions govern. Profiles and unspecified construction are diagrammatic.

THE ARK / AN ILLUSTRATED ANATOMY

# HULL / EXPLODED AXONOMETRIC STUDY

A diagram of the three-story wooden vessel. Vertical separation is expanded to expose the decks.

## 01 TIMBER ROOF / THREE DECK PLANES

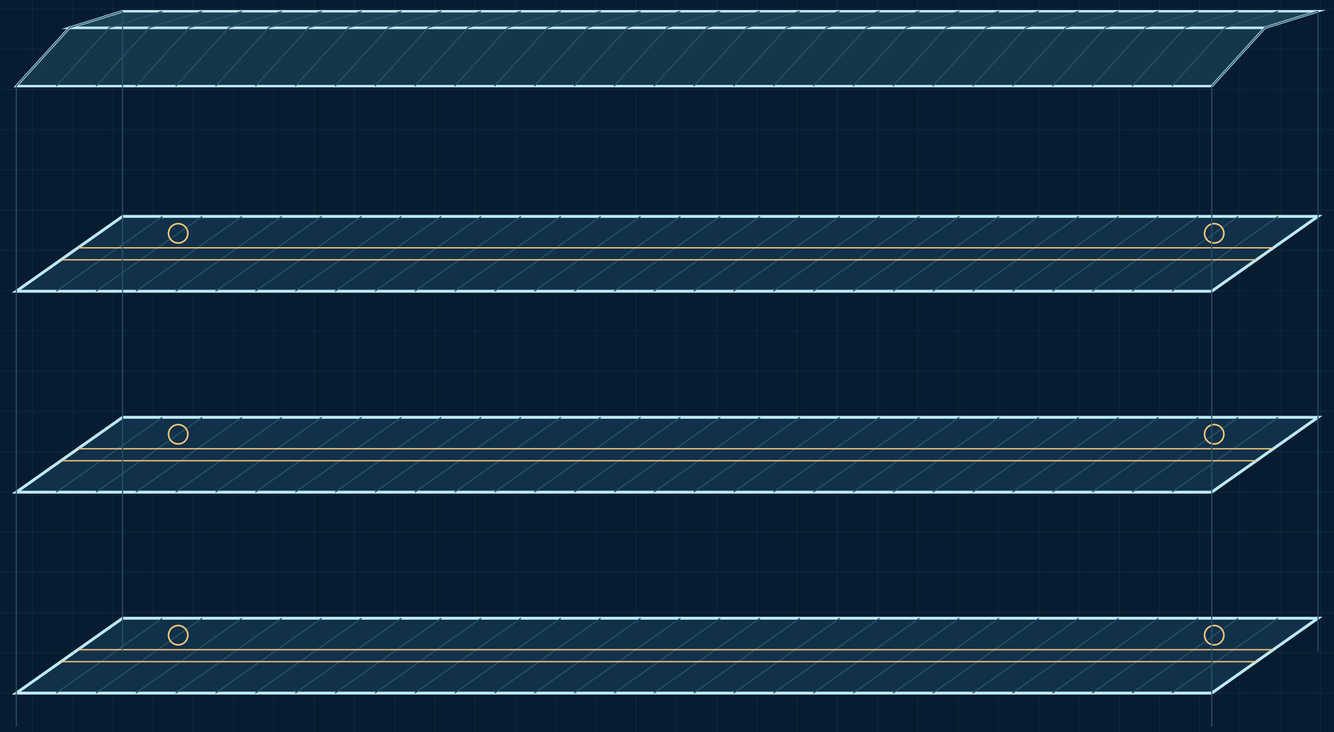

**UPPER FLOOR**
H-z 31 ft 6 in

**MIDDLE FLOOR**
H-z 16 ft 6 in

**LOWER FLOOR**
H-z 1 ft 6 in

AMBER LINES: 12 ft central aisle. CIRCLES: stair locations. Deck edges show the outside envelope.

Rectangular bounding planes simplify the atlas rounded ends; deck outline trimming is not specified.

### MEASURED COMPONENTS

450 x 75 ft exterior plan
30 frame bays at 15 ft pitch
Three ordinary floor levels
1 ft 6 in side/end allowance

### EXPLODED VIEW

Decks are separated for visibility.
Spacing shown is not deck height.
The actual floor elevations appear beside each plane and on A-05.

### WOODEN SYSTEM

Timber deck members and ribs
Wooden pegs / splines / wedges
No metal fasteners or concealed metal structure in the Ark.

### DRAWING STATUS

Measured architectural illustration.
Roof sections, member sizing and board widths are diagrammatic.
Source geometry stays distinct from the larger linked carrier.

**BRIAN CHAPMAN SR MSP A+ CIW**

Source: The Ark: An Illustrated Anatomy | Chapters 3-7 | 1 cubit = 18 in = 1.5 ft

Fictional architectural study. Written dimensions govern. Profiles and unspecified construction are diagrammatic.

**A-06**

REV 01 / 17 OCT 2026